



District : Erode
Taluk : Perundurai
Village : Kandampalayam [16]

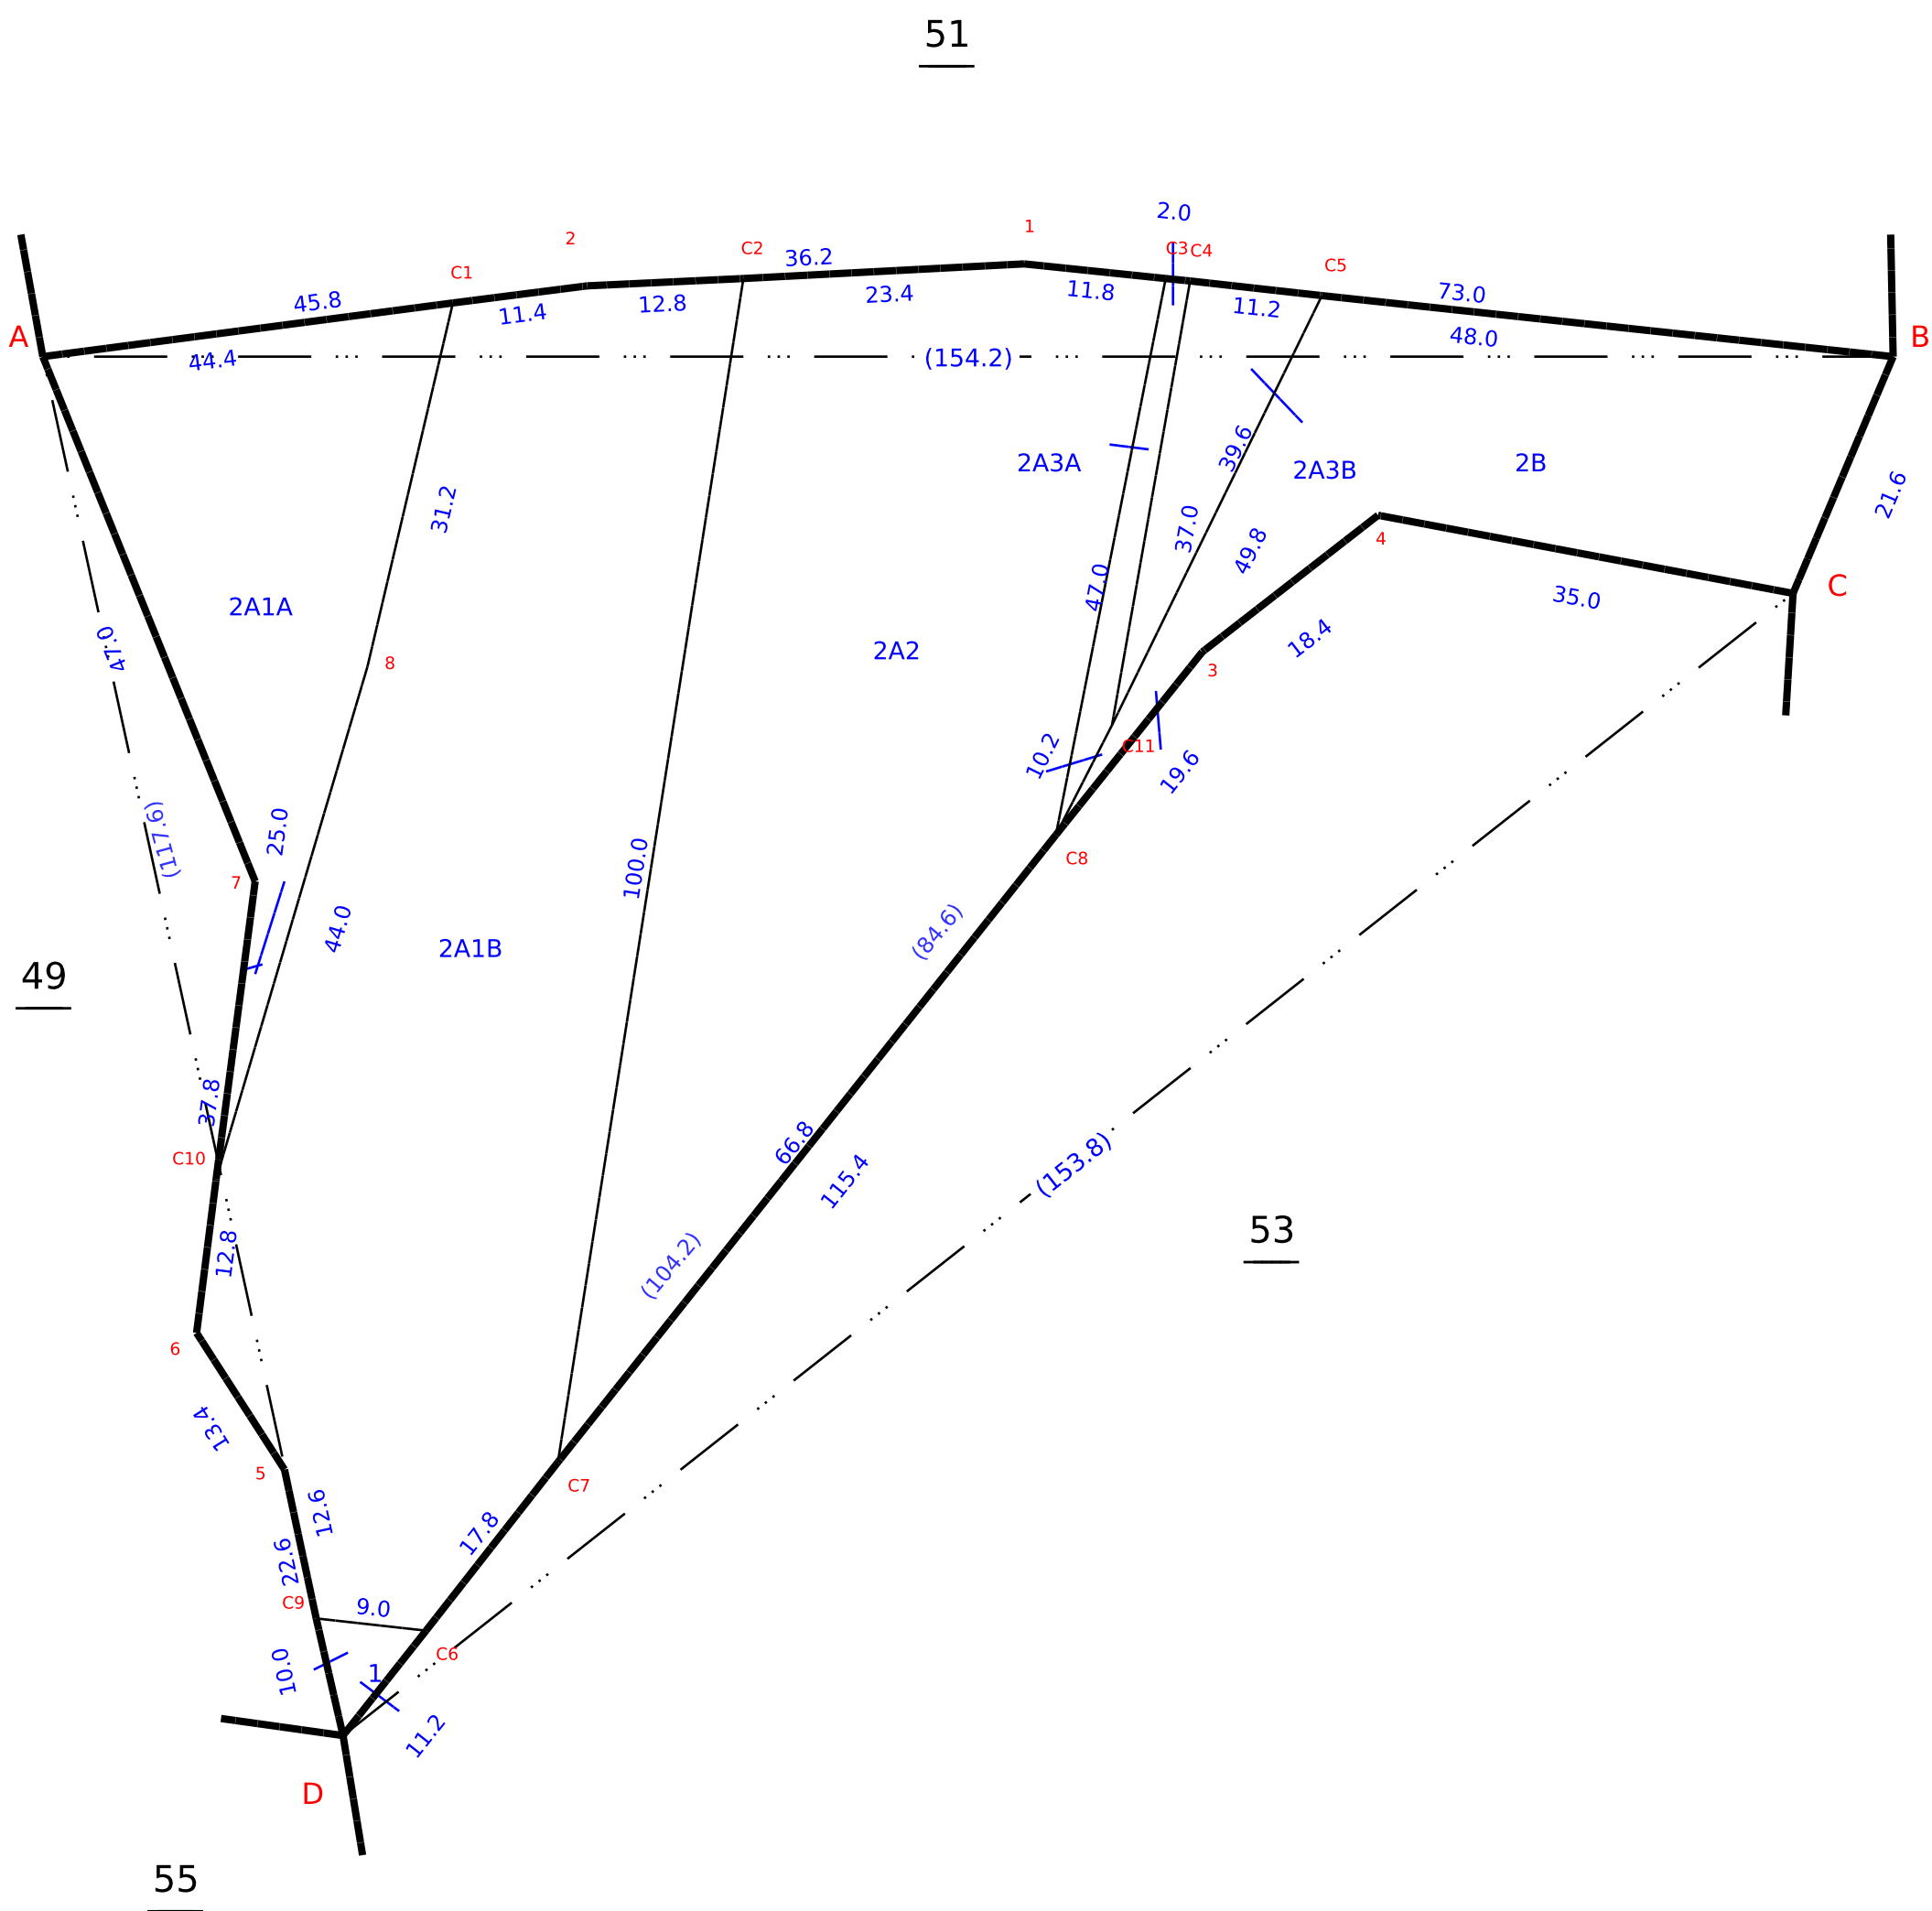

Survey No : 52
Area : Hect 00 Ares 77.50
Scale : 1 : 576

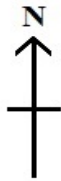

V.N0.49
NASIYANUR